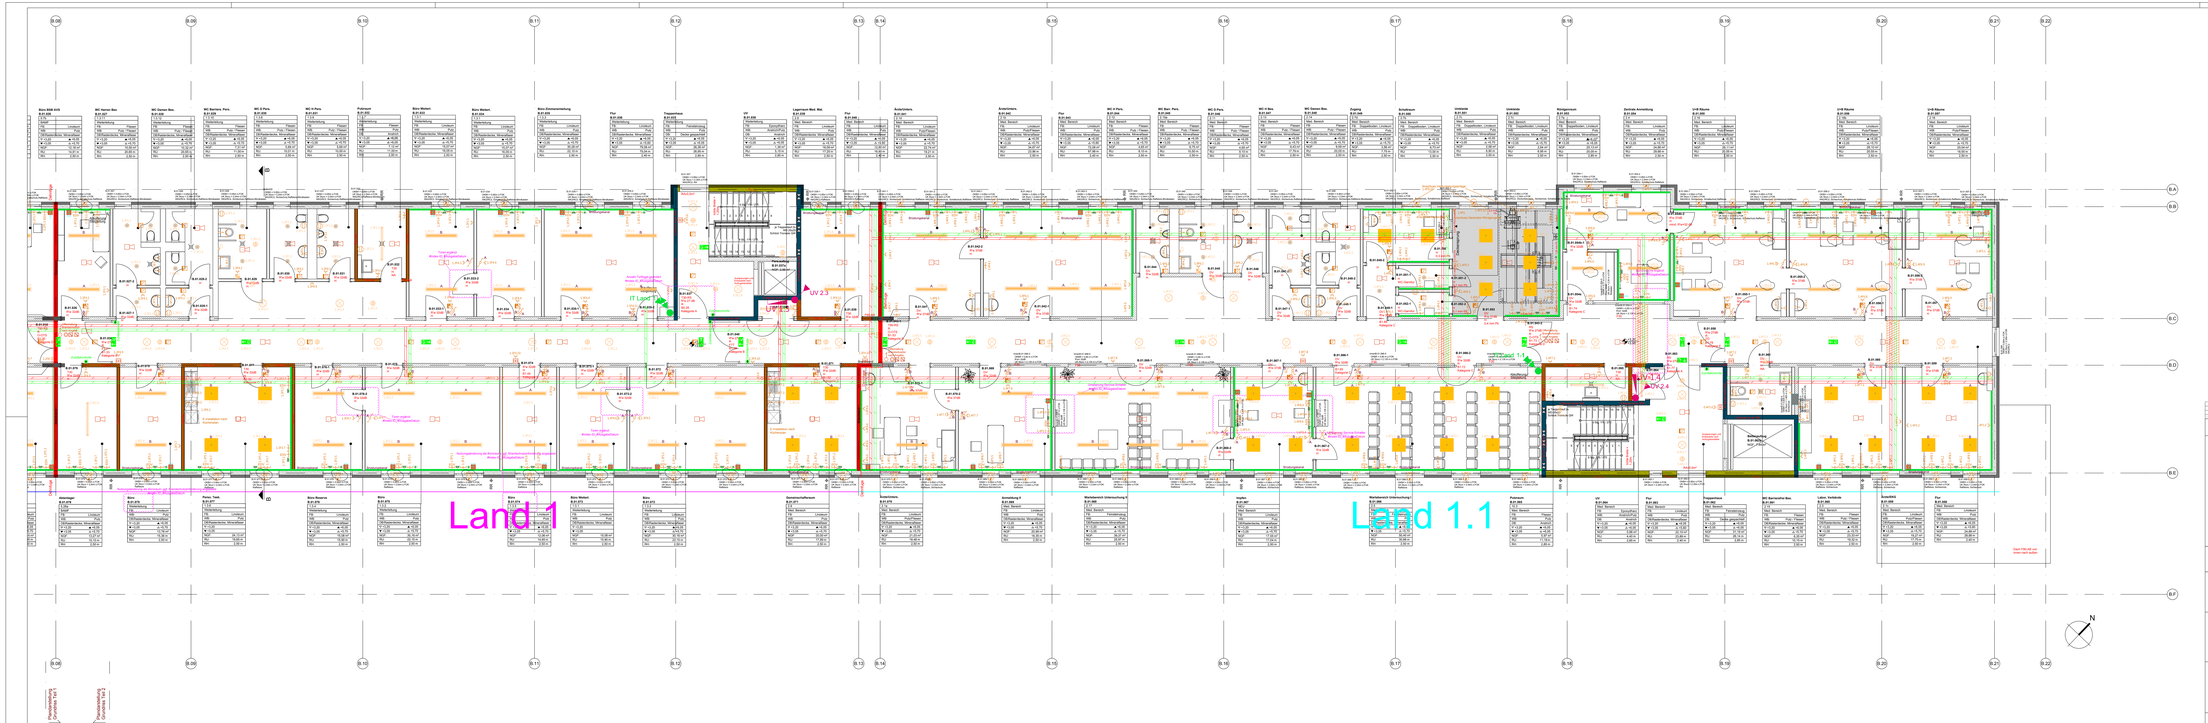

Änderungsnummer	Datum	Name
1	27.08.19	Ki
2	15.05.19	Ki

Plan-Nr.: HA_B_ELI_B_1G_321_2_V

Index: _2_V

LAGEPLAN ÜBERGESCHOSS

Neubau der Erstaufnahmeeinrichtung (EAE) für Asylbewerber in der ehem. Bäuwarenkaserne Regensburg

GEB.:

Bauteil B

Lphß

GRUNDRISS 1.OBERGESCHOSS

MONTAGEPLANUNG

M 1:50

Elektroinstallation

BRGEN. AM:	GEZ.:	GENEHTIGTE:	GEZ.IN:	GEZ. AM:	BEARBEITET:	PLOTDATUM:	GRBNTRAG:
13.03.0	0.02	1.00.0		0000			

AUFTRAG

REGIERUNG DER OBERPFALZ
SACHGEBIET BAUWESEN
Postfach 110 061
93049 Regensburg

ARCHITEKTEN DES ANTRAGSTELLERS

ARGE
EAE REGENSBURG
Bittner Hochbau GmbH - Ziegetsberger Straße 1
Winzerhofer Straße 5
Weiherstraße 1

ARCHITEKT

STÄDELI ARCHITEKTEN
Architekten und Stadtplaner
Bodenseestr. 25 D-81241 München
Tel.: 089 / 20 20 20 - 0 Fax: 089 / 20 20 20 - 20
info@staedeli-architekten.de
www.staedeli.eu

Planung

ARGE
HOCHBAUTEILE ARCHITEKTEN
Bittner Hochbau GmbH
Ziegetsberger Str. 5a/1/2
D-93051 Regensburg
Tel. 0941 58 48 0
Fax. 0941 58 48 20
hochbau@ziegetsberger.de
www.bittner-arbeitsgruppe.de

ZIEGA

AUTO

HA_B_ELI_B_XX_300_1_V